



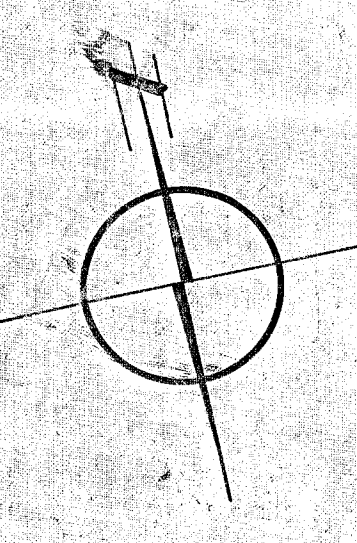

ESCALA 1:1000

s/m. Mas propiedad de A. ADEN Y E. AYALA

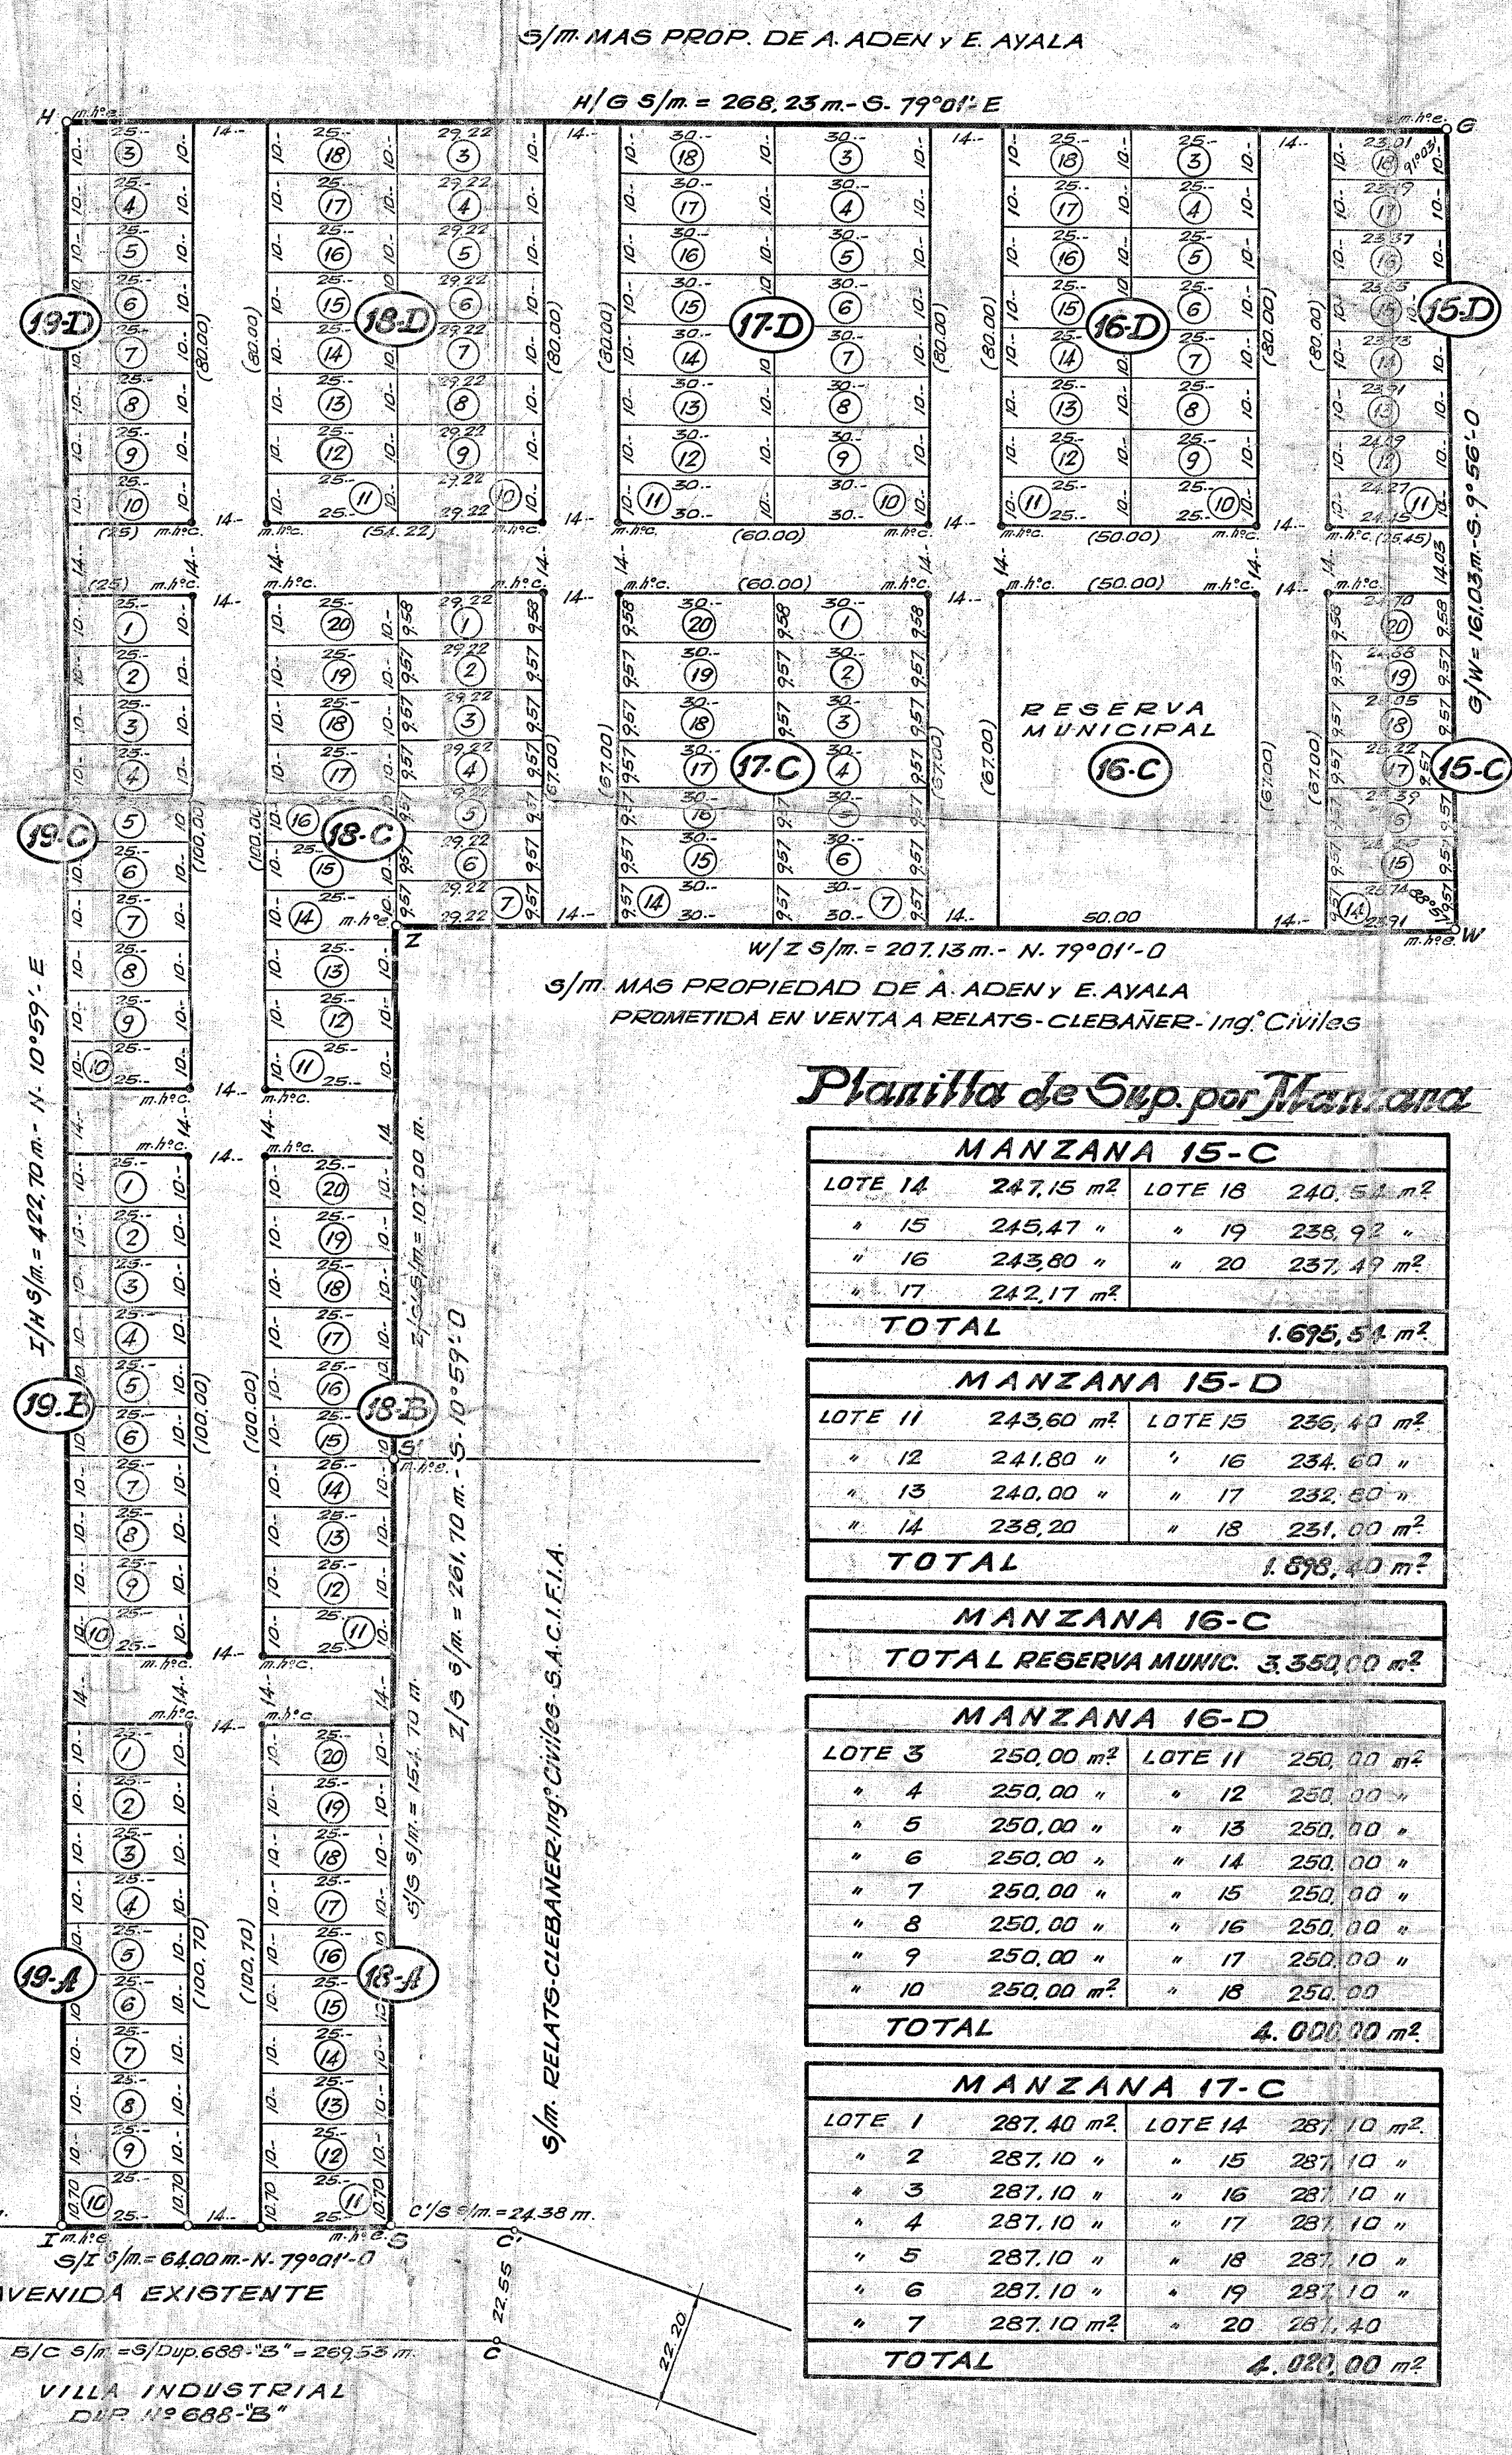

s/m. MAS PROP. DE A. ADEN Y E. AYALA

H/G s/m = 268,25 m - S. 79°01' E

W/Z s/m = 207,13 m - N. 79°01' O

s/m. MAS PROPIEDAD DE A. ADEN Y E. AYALA
PROMETIDA EN VENTA A RELATS-CLEBAÑER Ing. Civiles

Planilla de Sup. por Manzana

MANZANA 15-C			
LOTE 14	247,15 m²	LOTE 18	240,51 m²
" 15	245,47 "	" 19	238,92 "
" 16	243,80 "	" 20	237,49 m²
" 17	242,17 m²		
TOTAL		1.695,54 m²	

MANZANA 15-D			
LOTE 11	243,60 m²	LOTE 15	236,43 m²
" 12	241,80 "	" 16	234,60 "
" 13	240,00 "	" 17	232,80 "
" 14	238,20 "	" 18	231,00 m²
TOTAL		1.695,40 m²	

MANZANA 16-C	
TOTAL RESERVA MUNIC. 3.350,00 m²	

MANZANA 16-D			
LOTE 3	250,00 m²	LOTE 11	250,00 m²
" 4	250,00 "	" 12	250,00 "
" 5	250,00 "	" 13	250,00 "
" 6	250,00 "	" 14	250,00 "
" 7	250,00 "	" 15	250,00 "
" 8	250,00 "	" 16	250,00 "
" 9	250,00 "	" 17	250,00 "
" 10	250,00 m²	" 18	250,00 "
TOTAL		4.000,00 m²	

MANZANA 17-C			
LOTE 1	287,40 m²	LOTE 14	287,10 m²
" 2	287,10 "	" 15	287,10 "
" 3	287,10 "	" 16	287,10 "
" 4	287,10 "	" 17	287,10 "
" 5	287,10 "	" 18	287,10 "
" 6	287,10 "	" 19	287,10 "
" 7	287,10 m²	" 20	287,40 "
TOTAL		4.020,00 m²	

s/m. J. J. JUAN JOSE Y JULIO JOSE A. DE LOS SANTOS

MANZANA 17-D			
LOTE 3	300,00 m²	LOTE 11	300,00 m²
" 4	300,00 "	" 12	300,00 "
" 5	300,00 "	" 13	300,00 "
" 6	300,00 "	" 14	300,00 "
" 7	300,00 "	" 15	300,00 "
" 8	300,00 "	" 16	300,00 "
" 9	300,00 "	" 17	300,00 "
" 10	300,00 m²	" 18	300,00 "
TOTAL		4.800,00 m²	

MANZANA 18-A			
LOTE 11	267,50 m²	LOTE 16	250,00 m²
" 12	250,00 "	" 17	250,00 "
" 13	250,00 "	" 18	250,00 "
" 14	250,00 "	" 19	250,00 "
" 15	250,00 "	" 20	250,00 "
TOTAL		2.517,50 m²	

MANZANA 18-B			
LOTE 1	250,00 m²	LOTE 16	250,00 m²
" 12	250,00 "	" 17	250,00 "
" 13	250,00 "	" 18	250,00 "
" 14	250,00 "	" 19	250,00 "
" 15	250,00 "	" 20	250,00 "
TOTAL		2.500,00 m²	

MANZANA 18-C			
LOTE 1	279,95 m²	LOTE 13	250,00 m²
" 2	279,64 "	" 14	250,00 "
" 3	279,64 "	" 15	250,00 "
" 4	279,64 "	" 16	250,00 "
" 5	279,64 "	" 17	250,00 "
" 6	279,64 "	" 18	250,00 "
" 7	279,64 "	" 19	250,00 "
" 11	250,00 "	" 20	250,00 "
" 12	250,00 "		
TOTAL		4.457,77 m²	

MANZANA 18-D			
LOTE 3	292,20 m²	LOTE 11	250,00 m²
" 4	292,20 "	" 12	250,00 "
" 5	292,20 "	" 13	250,00 "
" 6	292,20 "	" 14	250,00 "
" 7	292,20 "	" 15	250,00 "
" 8	292,20 "	" 16	250,00 "
" 9	292,20 "	" 17	250,00 "
" 10	292,20 "	" 18	250,00 "
TOTAL		4.337,60 m²	

MANZANA 19-A			
LOTE 1	250,00 m²	LOTE 6	250,00 m²
" 2	250,00 "	" 7	250,00 "
" 3	250,00 "	" 8	250,00 "
" 4	250,00 "	" 9	250,00 "
" 5	250,00 "	" 10	267,50 "
TOTAL		2.517,50 m²	

MANZANA 19-B			
LOTE 1	250,00 m²	LOTE 6	250,00 m²
" 2	250,00 "	" 7	250,00 "
" 3	250,00 "	" 8	250,00 "
" 4	250,00 "	" 9	250,00 "
" 5	250,00 "	" 10	250,00 "
TOTAL		2.500,00 m²	

MANZANA 19-C			
LOTE 1	250,00 m²	LOTE 6	250,00 m²
" 2	250,00 "	" 7	250,00 "
" 3	250,00 "	" 8	250,00 "
" 4	250,00 "	" 9	250,00 "
" 5	250,00 "	" 10	250,00 "
TOTAL		2.500,00 m²	

MANZANA 19-D			
LOTE 3	250,00 m²	LOTE 7	250,00 m²
" 4	250,00 "	" 8	250,00 "
" 5	250,00 "	" 9	250,00 "
" 6	250,00 "	" 10	250,00 "
TOTAL		2.000,00 m²	


SUMA TOTAL DE 153 LOTES 43.094,41 m²
SUMA DE CALLES 17.072,87 m²
TOTAL FRACCION THGWZSI 60.167,28 m²
TOTAL FRACCION THGWZSI "3 DUP 4043-U" 60.167,28 m²

NOTA:
Medidas en metros.
Angulos no especificos: rectos o suplementarios.
m.h.c.: Mojon hormigon colocado.
m.h.e.: Mojon hormigon existente.

Nota: Unificac. y Division Lote 11 de la Manz. 19/B con el lote 11 de la Manz. 19/A. Ver Plan N° 2255-11.

OBJETO: DIVISION DE LA FRACCION THGWZSI "3 DUP 4043-U" DUR DE MENSURA EN BASE AL DUPL. N° 4043-11
CARACTER: PARTICULAR
PROVINCIA DE CORRIENTES- REP. ARG.
DEPARTAMENTO: CAPITAL
LUGAR: MUNICIPIO DE CORRIENTES
PROPIEDAD DE:

"GUARANI" S.A.C.I.F.I.E.
UBICACION: MANZANA N° 20- PARAJE "BAÑADO NORTE"
DOMINIO: Reg. Prop. Capital: T° 2- F° 259, N° 229- Año 1974-
Reg. Prop. Municip: T° 2- L° 8- F° 268- Fed. 247- Año 1974-
ADREMA: A1- 2186-2
Duplicado relacionado: N° 4043-11

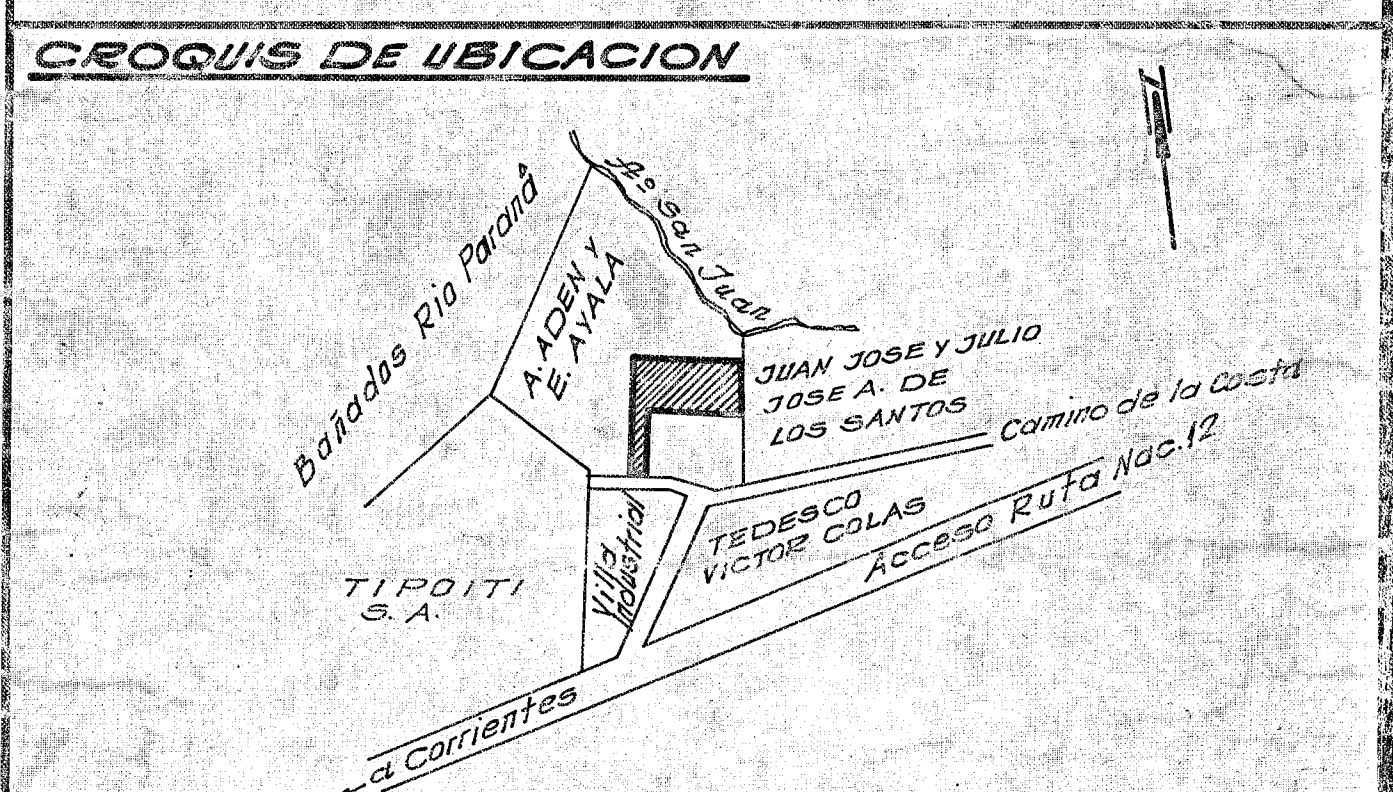

CORRIENTES, 23 DE DICIEMBRE DE 1975.-

AMERICO JACOBACCI
Agente Nacional
Matric. N° 147. C. Prof. N° 8
Dom.: Av. España 2002. Ctes.-
JUAN CARLOS RELATS
Ingeniero Civil
L.E. N° 6.011.163
por: Guarani S.A.C.I.F.I.E.